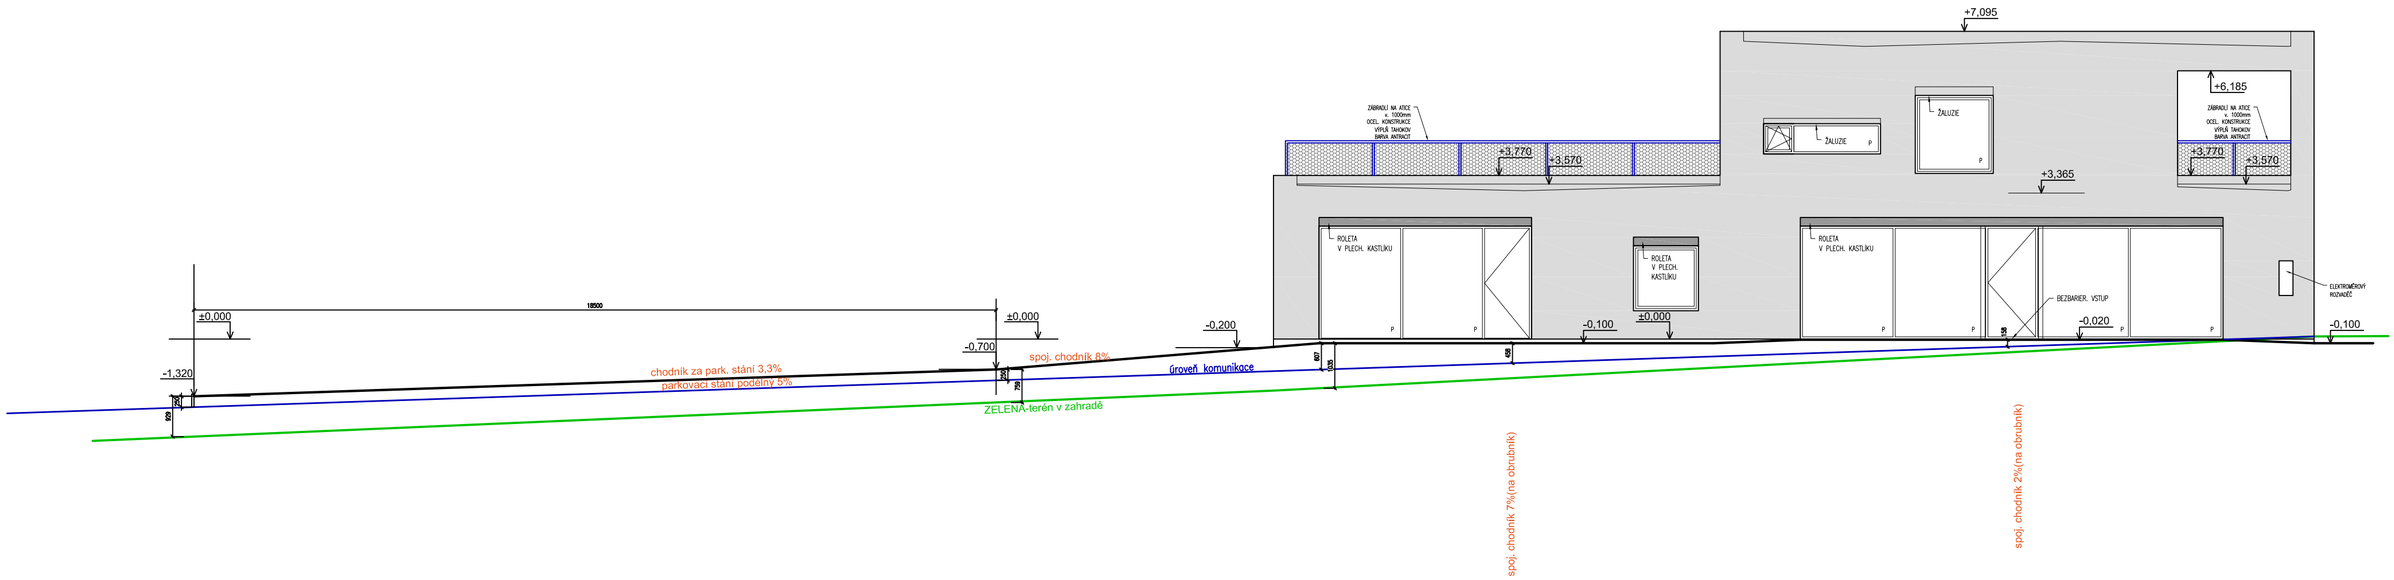

+7,095
+6,185
ŽALUZIE
ŽALUZIE
P
ZÁBRADLÍ NA ATIKE
v. 1000mm
OCEL. KONSTRUKCE
VÝPLŇ TAHOKOV
BARVA ANTRACIT
+3,770
+3,570
+3,365
ROLETA
V PLECH. KASTLÍKU
-0,200
-0,100
±0,000
-0,020
BEZBARIER. VSTUP
ELEKTROMĚROVÝ
ROZVAŘEČ
18500
-0,700
-1,320
chodník za park. stání 3,3%
parkovací stání podélný 5%
spoj. chodník 8%
Groveň komunikace
ZELENÁ-terén v zahradě
spoj. chodník 7%(na obrubník)
spoj. chodník 2%(na obrubník)