
SITUACE M 1:200

VSTUPY DO OBJEKTU
46/32 Č. PARCEL
HRANICE PARCEL – KATASTRÁLNÍ MAPA
HRANICE ŘEŠENÉHO ÚZEMÍ
STÁVAJÍCÍ DRÁTĚNÉ OPLOCENÍ POZEMKU v. 1,60m
ODSTRANĚNÉ OPLOCENÍ POZEMKU
NOVÉ DOPOJENÍ DRÁTĚNÉHO OPLOCENÍ v. 1,60m

STÁVAJÍCÍ OKOLNÍ PLOCHY
- okolní stavby
- stávající skleník
- komunikace (živice)
- chodník (betonová dlažba)
- zeleň
- zpevněné plochy (na soukromém pozemku)

PLOCHY POZEMKU STAVBY
- PŘEDMĚTNÝ NOVÝ OBJEKT
- CHODNÍK (propustná dlažba Godelmann Geoston)
- VAROVNÝ BEZPEČNOSTNÍ PÁS š.400mm
- ZATRAVŇOVACÍ TVAROVKY/ZATRAVNĚNÁ PLOCHA
- TRAVNATÉ PLOCHY

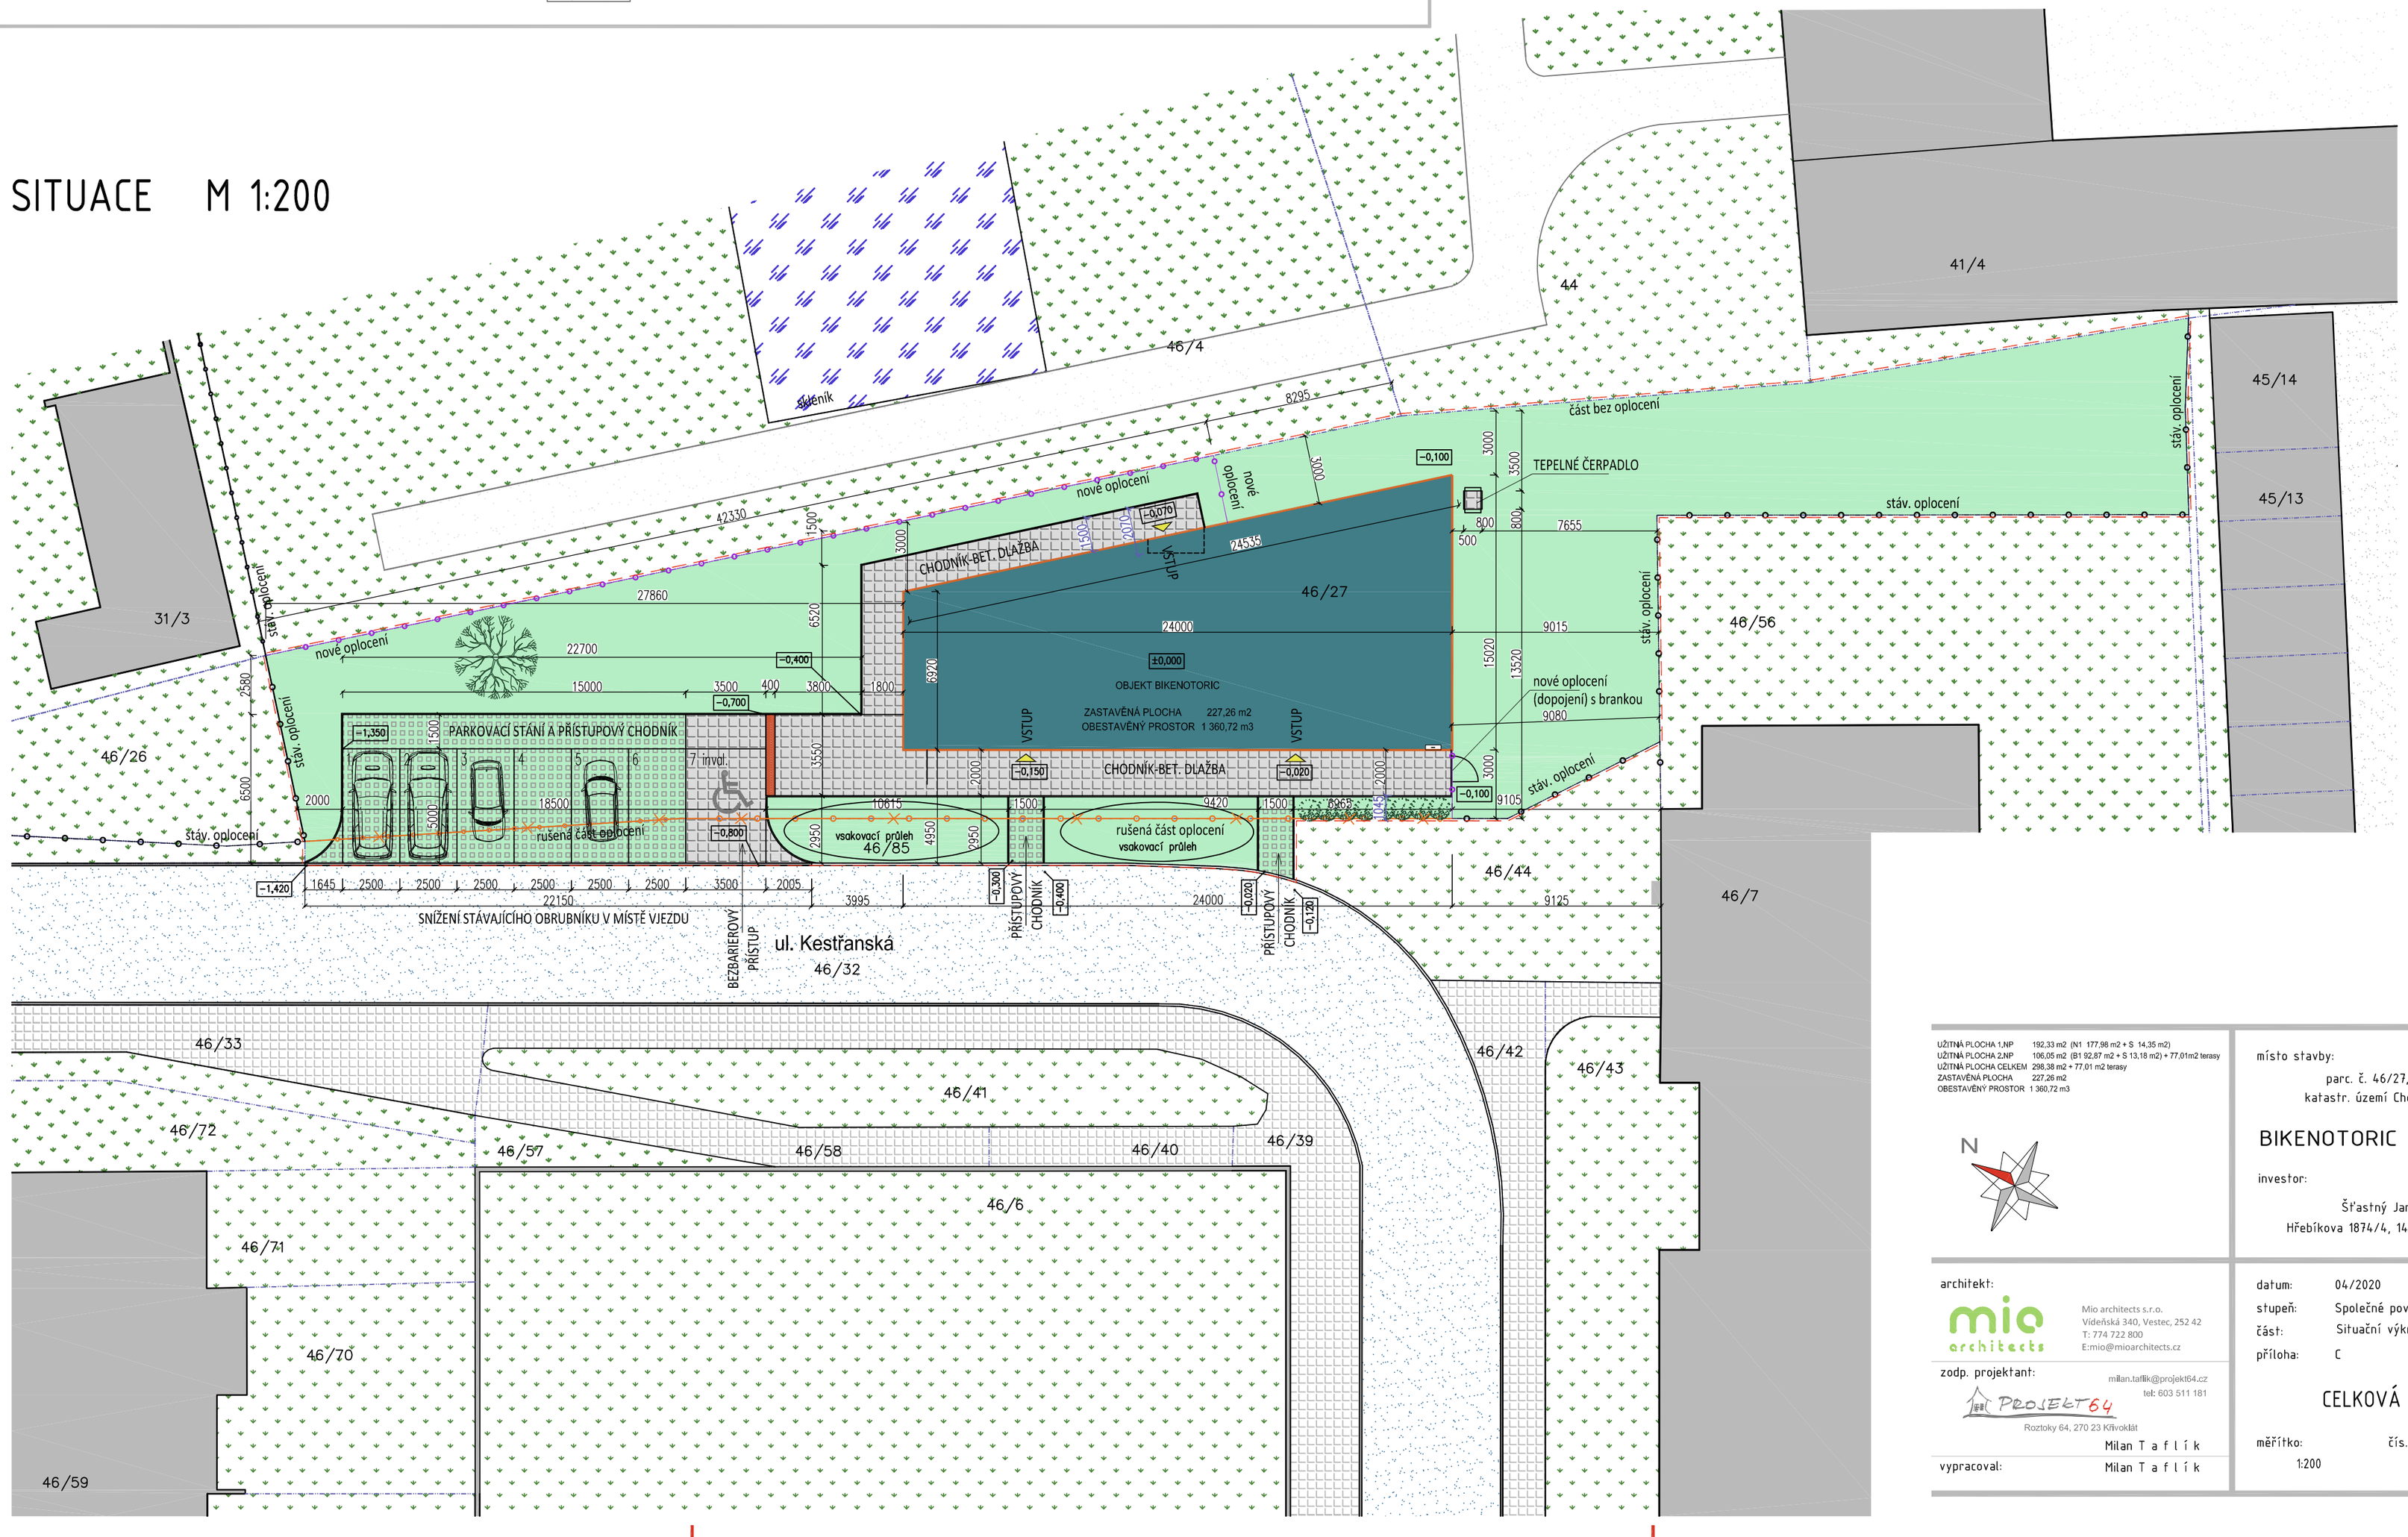

UŽITNÁ PLOCHA 1.NP	192,33 m2 (N1 177,98 m2 + S 14,35 m2)
UŽITNÁ PLOCHA 2.NP	106,05 m2 (B1 92,87 m2 + S 13,18 m2) + 77,01m2 terasy
UŽITNÁ PLOCHA CELKEM	298,38 m2 + 77,01 m2 terasy
ZASTAVĚNÁ PLOCHA	227,26 m2
OBESTAVĚNÝ PROSTOR	1 360,72 m3

místo stavby:
parc. č. 46/27, 46/85
katastr. území Cholupice [652393]

BIKENOTORIC PÍSNICE

investor:
Šťastný Jan
Hřebíkova 1874/4, 143 00 Praha 4

architekt:
mio architects
Mio architects s.r.o.
Vídeňská 340, Vestec, 252 42
T: 774 722 800
E:mio@mioarchitects.cz

zodp. projektant:
milan.taflik@projekt64.cz
tel: 603 511 181
PROJEKT64
Roztoky 64, 270 23 Křivoklát
Milan T a f l í k

vypracoval: Milan T a f l í k

datum: 04/2020
stupeň: Společné povolení
část: Situační výkresy
příloha: C

CELKOVÁ SITUACE

měřítko: 1:200
čís. výkresu: C.03